

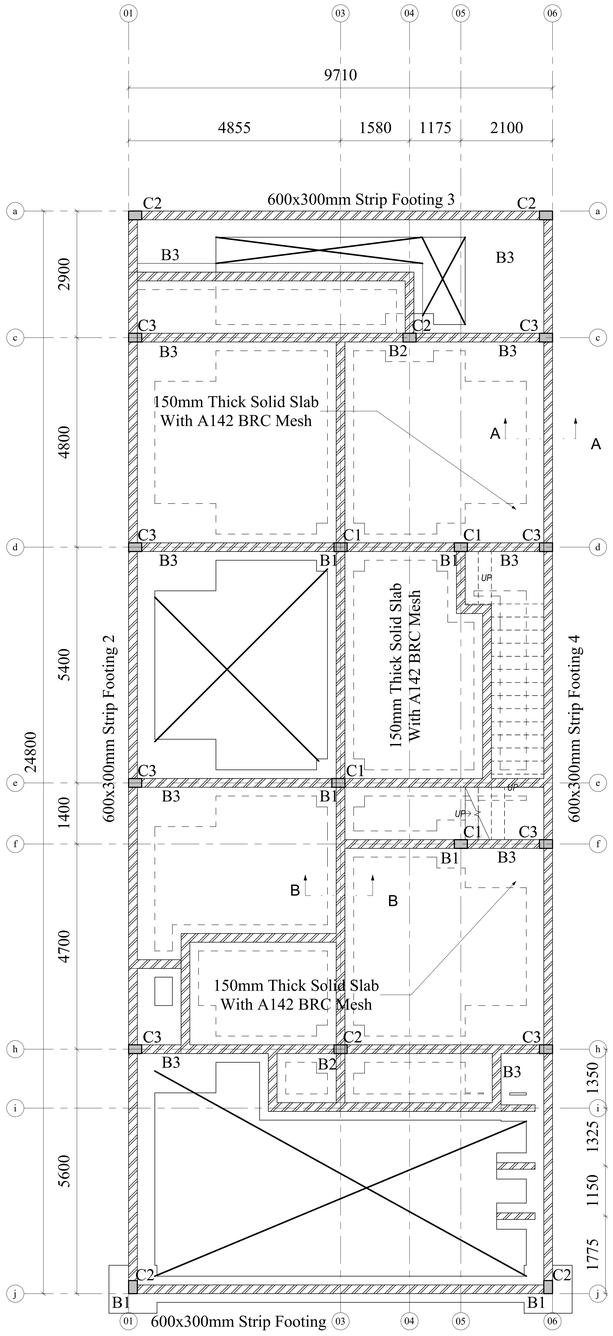


GROUND FLOOR LAYOUT
1 : 50

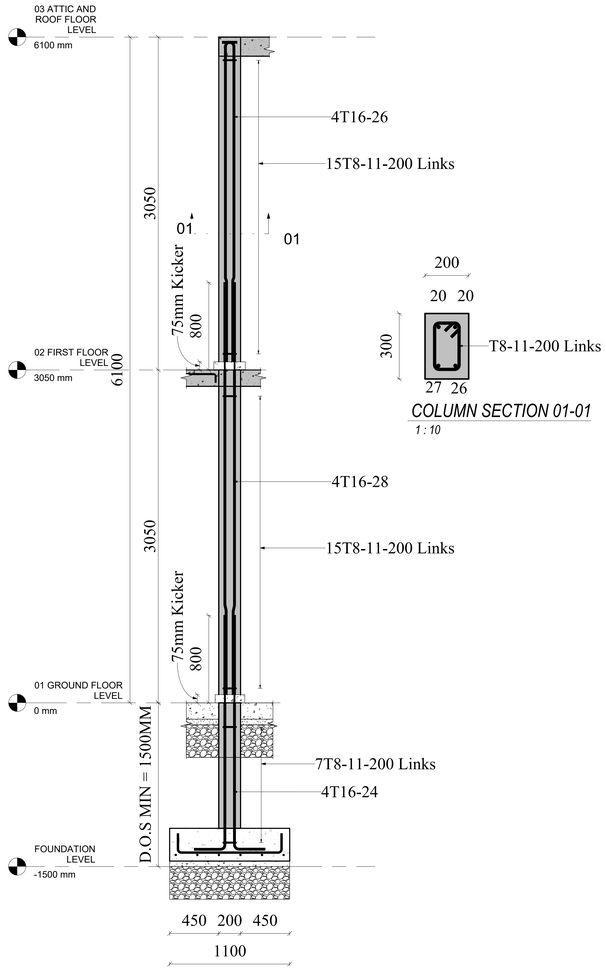


COLUMN C1
1 : 20


COLUMN SECTION 01-01
1 : 10

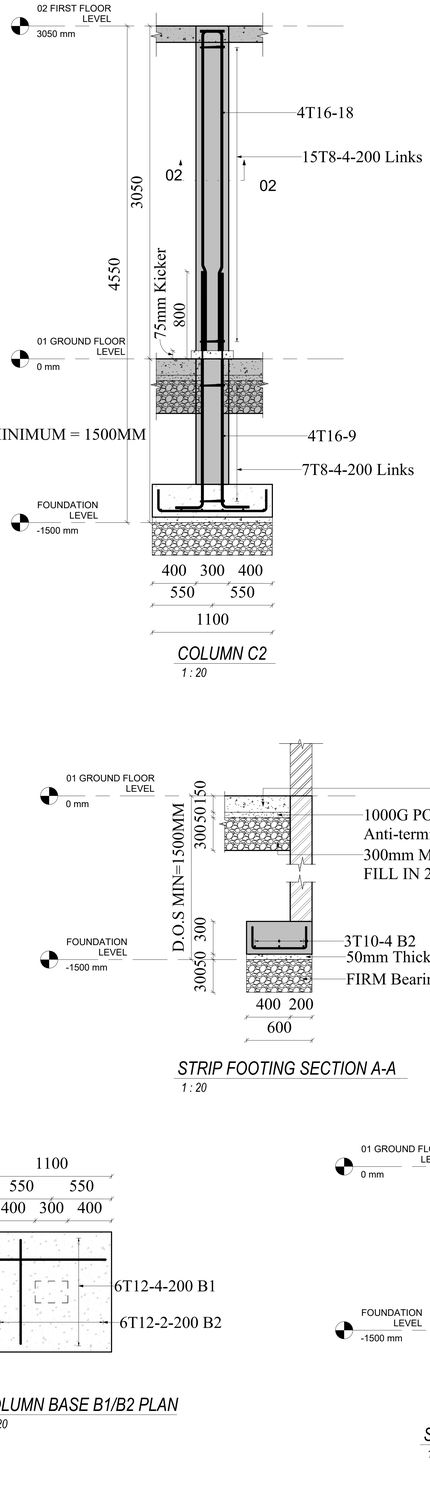


COLUMN C2
1 : 20

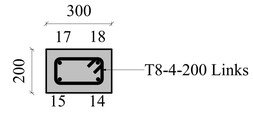


COLUMN SECTION 02-02
1 : 10

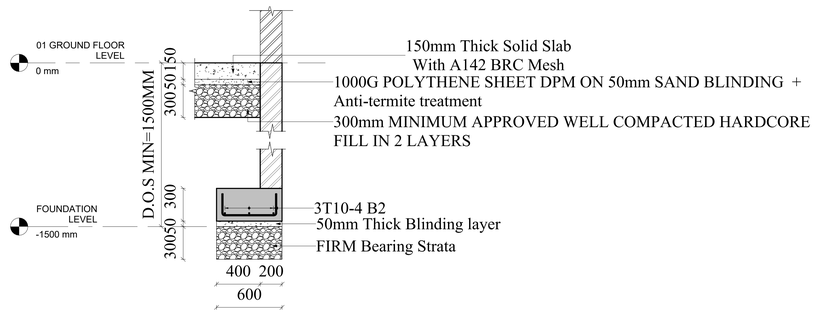


STRIP FOOTING SECTION A-A
1 : 20

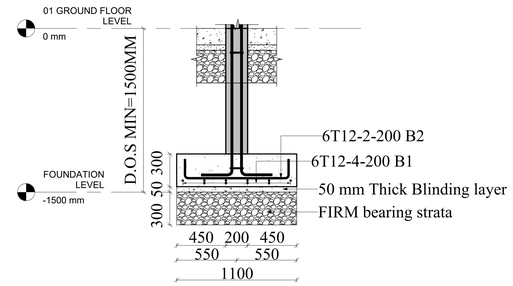

COLUMN BASE B1/B2
1 : 20

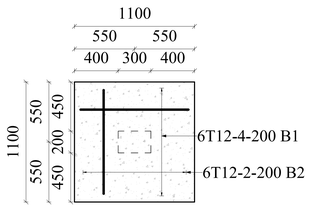

COLUMN BASE B1/B2 PLAN
1 : 20

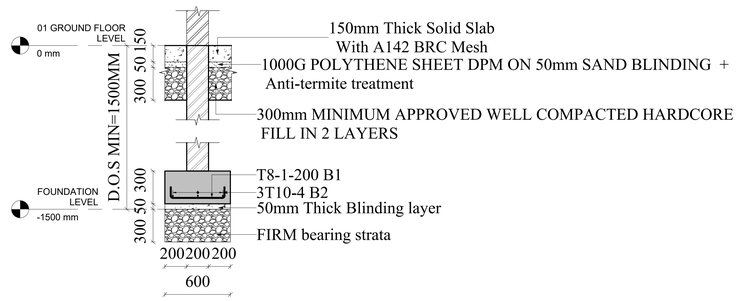

STRIP FOOTING SECTION B-B
1 : 20

GENERAL STRUCTURAL NOTES

1. All dimensions in millimeters.
2. Figured dimensions to be taken from the drawing. Do not scale.
3. All structural drawings are to be read in conjunction with their relevant counterparts, including but not limited to architectural, mechanical, electrical and plumbing drawings. Any discrepancy to be reported to the Engineer immediately.
4. All excavations are to be approved by the Civil and Structural Engineer(s).
5. Concrete to be class C20/25 with a minimum cube crushing strength of 18N/mm^2 and 25N/mm^2 at 7 days and 28 days respectively.
6. Blinding concrete to be class C15 with a minimum crushing strength of 15N/mm^2 at 28 days.
7. The minimum cover to reinforcement:
   - Foundations : 50mm
   - Columns : 40mm
   - Beams : 25mm
   - Slabs : 25mm
8. Hoop Iron to be placed on every other course of masonry walls and bonded to the reinforced concrete columns.
9. All reinforcement works to be inspected and approved by the Engineer before concreting.
10. Minimum spacing between longitudinal bars not less than 25mm.
11. Minimum spacing between transverse bars not less than 150mm c/c.
12. All segment lengths to be rounded up by 5mm and all cutting lengths to be rounded up by 50mm.
13. Reinforcement lap lengths to be 50 x Diameter of the smaller lapped bar.

T8 - 400mm	T20 - 1000mm
T10 - 500mm	T25 - 1200mm
T12 - 600mm	T32 - 1600mm
T16 - 800mm	

14. Masonry crushing strength to be 7 N/mm^2.
15. Compaction is to be done in layers not exceeding 150mm in thickness.
16. Waterproofing of Structures

- Approved and guaranteed waterproofing systems all as detailed shall be provided to the following structures:
  - Water tank slab

General Abbreviations as follows:

T - Top Bar	B - Bottom Bar
T1 - Main Top Bar	T2 - Distribution Top Bar
B1 - Main Bottom Bar	B2 - Distribution Bottom Bar
N.F - Near Face	F.F - Far Face
A/W - Alternating With	E.W. - Each Way

Revision	Description	Date

CLIENT: EVANS KAVISI & LATOYA OUNA


PROJECT: PROPOSED RESIDENTIAL DEVELOPMENT

ARCHITECT: DMS ARCHITECTURE


TITLE: FOUNDATION LAYOUT, COLUMN, COLUMN BASE AND STRIP FOOTING

ENG. LATOYA OUNA
E694


JOB No. 06	
DRG No. DMS-026-003/STR/00	
Project Date: JUNE 2026	
Sheet Issue Date: 15/06/2026	
DESIGNED: V.N.M	CHECKED BY: ENG. L.O
DRAWN BY: V.N.M	SCALE: As indicated

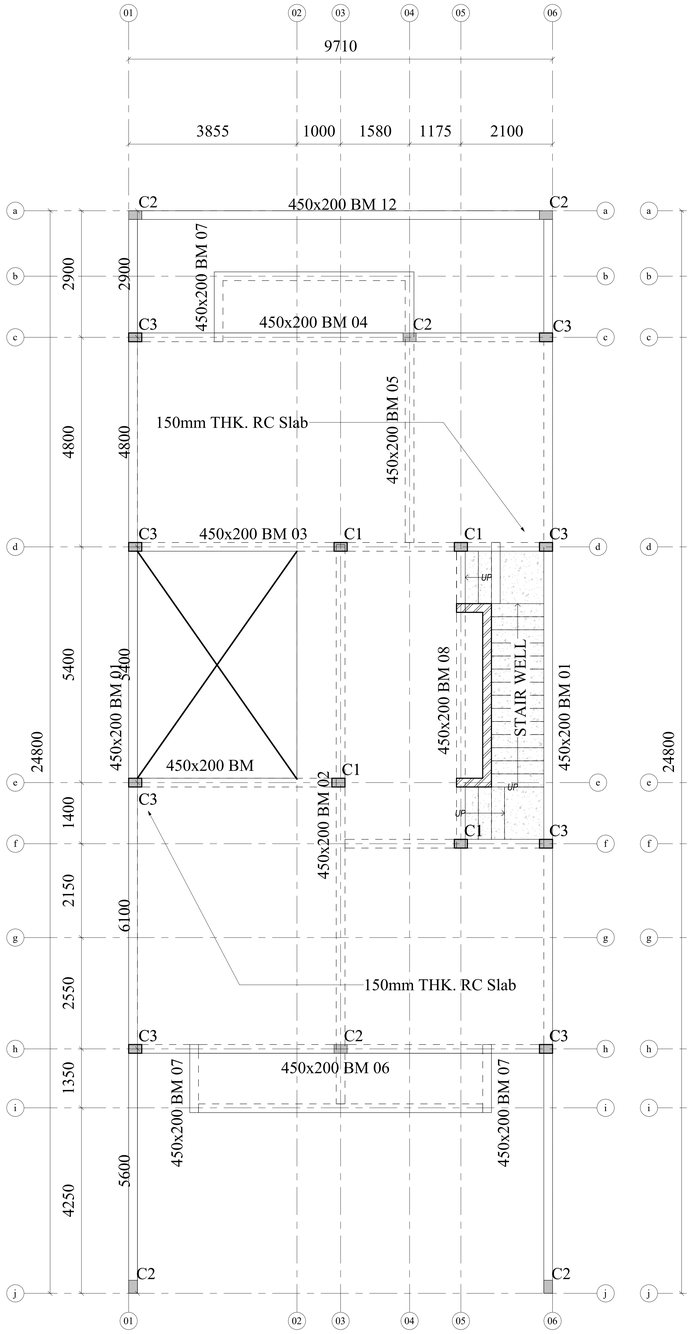


FIRST FLOOR LAYOUT
1 : 50

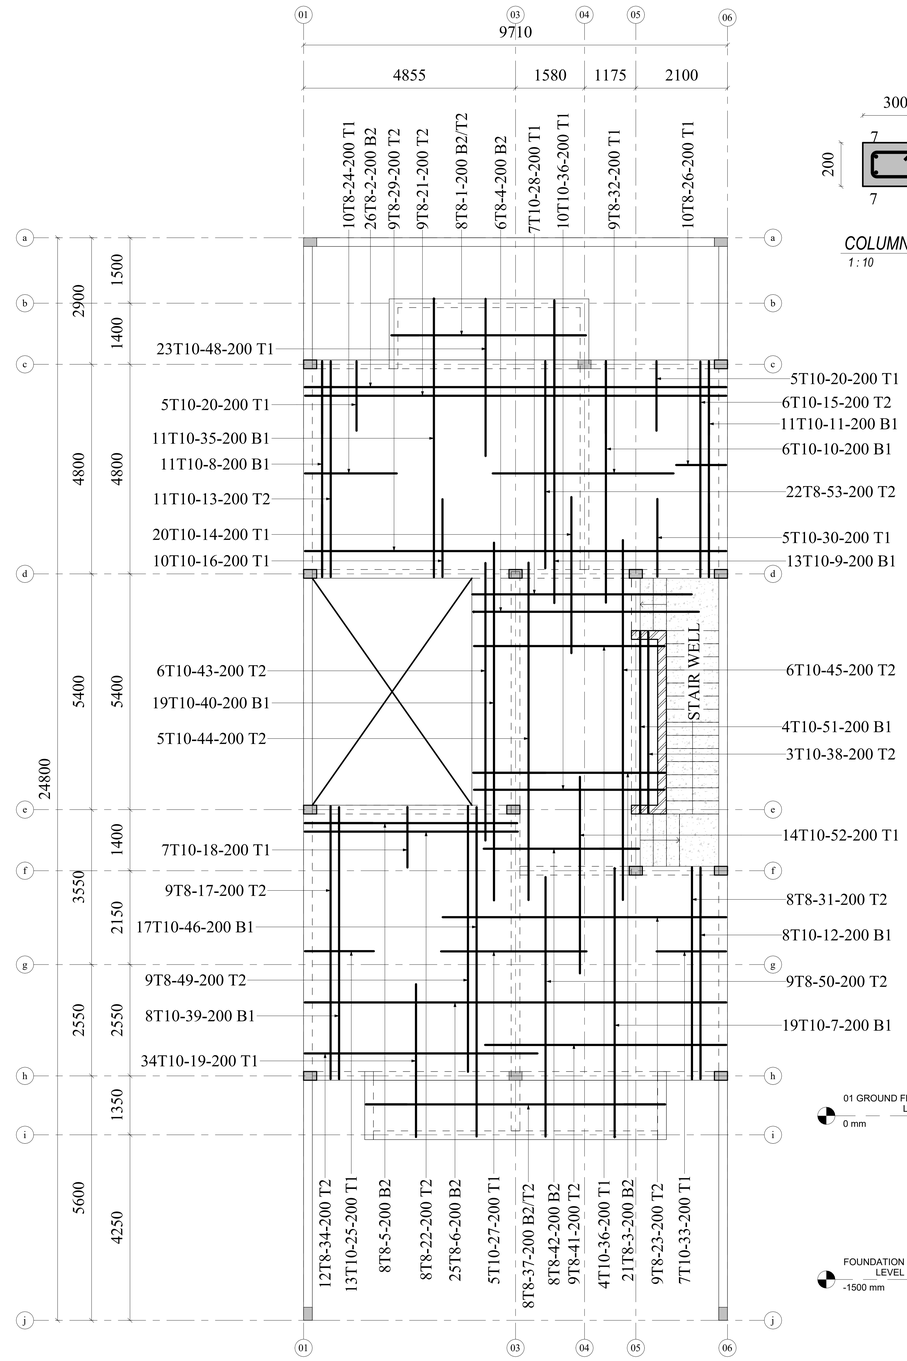


FIRST FLOOR REINFORCEMENT DETAILS
1 : 50

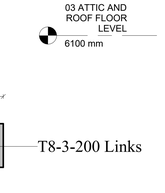


COLUMN SECTION 03-03
1 : 10

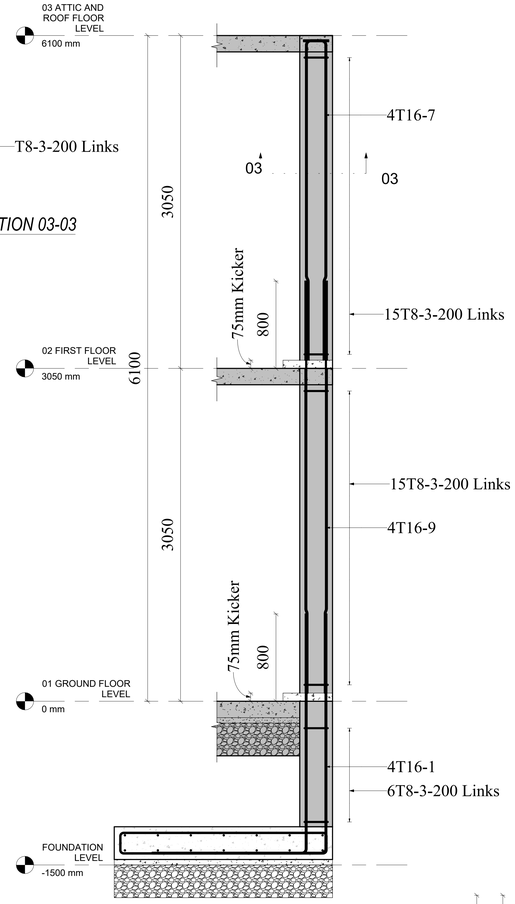

COLUMN C3
1 : 20

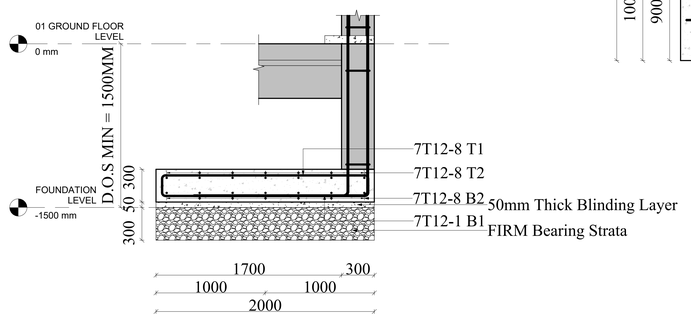

COLUMN BASE B3
1 : 20

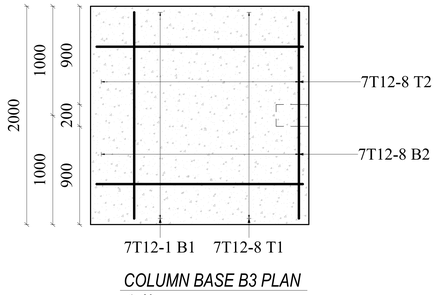

COLUMN BASE B3 PLAN
1 : 20

GENERAL STRUCTURAL NOTES

1. All dimensions in millimeters.
2. Figured dimensions to be taken from the drawing. Do not scale.
3. All structural drawings are to be read in conjunction with their relevant counterparts, including but not limited to architectural, mechanical, electrical and plumbing drawings. Any discrepancy to be reported to the Engineer immediately.
4. All excavations are to be approved by the Civil and Structural Engineer(s).
5. Concrete to be class C20/25 with a minimum cube crushing strength of 18N/mm^2 and 25N/mm^2 at 7 days and 28 days respectively.
6. Blinding concrete to be class C15 with a minimum crushing strength of 15N/mm^2 at 28 days.
7. The minimum cover to reinforcement:
   - Foundations : 50mm
   - Columns : 40mm
   - Beams : 25mm
   - Slabs : 25mm
8. Hoop Iron to be placed on every other course of masonry walls and bonded to the reinforced concrete columns.
9. All reinforcement works to be inspected and approved by the Engineer before concreting.
10. Minimum spacing between longitudinal bars not less than 25mm.
11. Minimum spacing between transverse bars not less than 150mm c/c.
12. All segment lengths to be rounded up by 5mm and all cutting lengths to be rounded up by 50mm.
13. Reinforcement lap lengths to be 50 x Diameter of the smaller lapped bar.
    - T8 - 400mm
    - T10 - 500mm
    - T12 - 600mm
    - T16 - 800mm
    - T20 - 1000mm
    - T25 - 1200mm
    - T32 - 1600mm
14. Masonry crushing strength to be 7 N/mm^2.
15. Compaction is to be done in layers not exceeding 150mm in thickness.
16. Waterproofing of Structures

- Approved and guaranteed waterproofing systems all as detailed shall be provided to the following structures:
  - Water tank slab

General Abbreviations as follows:

T - Top Bar	B - Bottom Bar
T1 - Main Top Bar	T2 - Distribution Top Bar
B1 - Main Bottom Bar	B2 - Distribution Bottom Bar
N.F - Near Face	F.F - Far Face
A/W - Alternating With	E.W. - Each Way

Revision	Description	Date

CLIENT: EVANS KAVISI & LATOYA OUNA

PROJECT: PROPOSED RESIDENTIAL DEVELOPMENT


ARCHITECT: DMS ARCHITECTURE

TITLE: FIRST FLOOR BEAM AND REINFORCEMENT LAYOUTS

ENG. LATOYA OUNA
E694


DESIGNED: V.N.M
DRAWN BY: V.N.M

JOB No. 06
DRG No. DMS-026-003/STR/01
Project Date: JUNE 2026
Sheet Issue Date: 15/06/2026
CHECKED BY: ENG. L.O
SCALE: As indicated

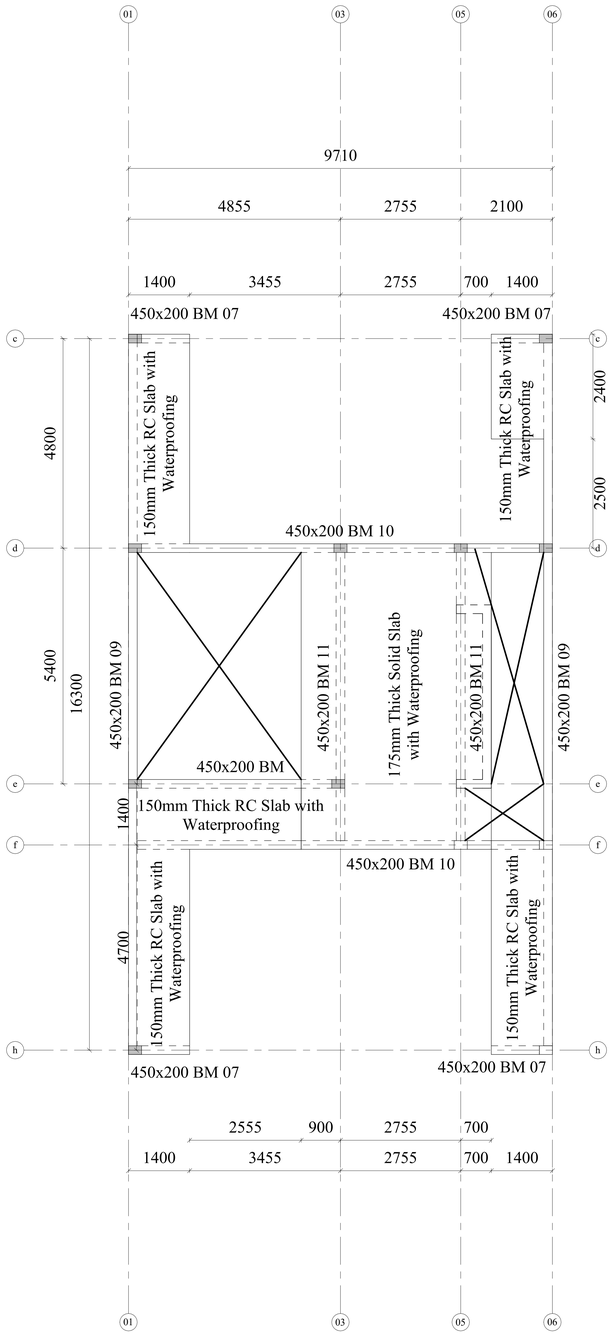

ATTIC FLOOR LAYOUT

1 : 50

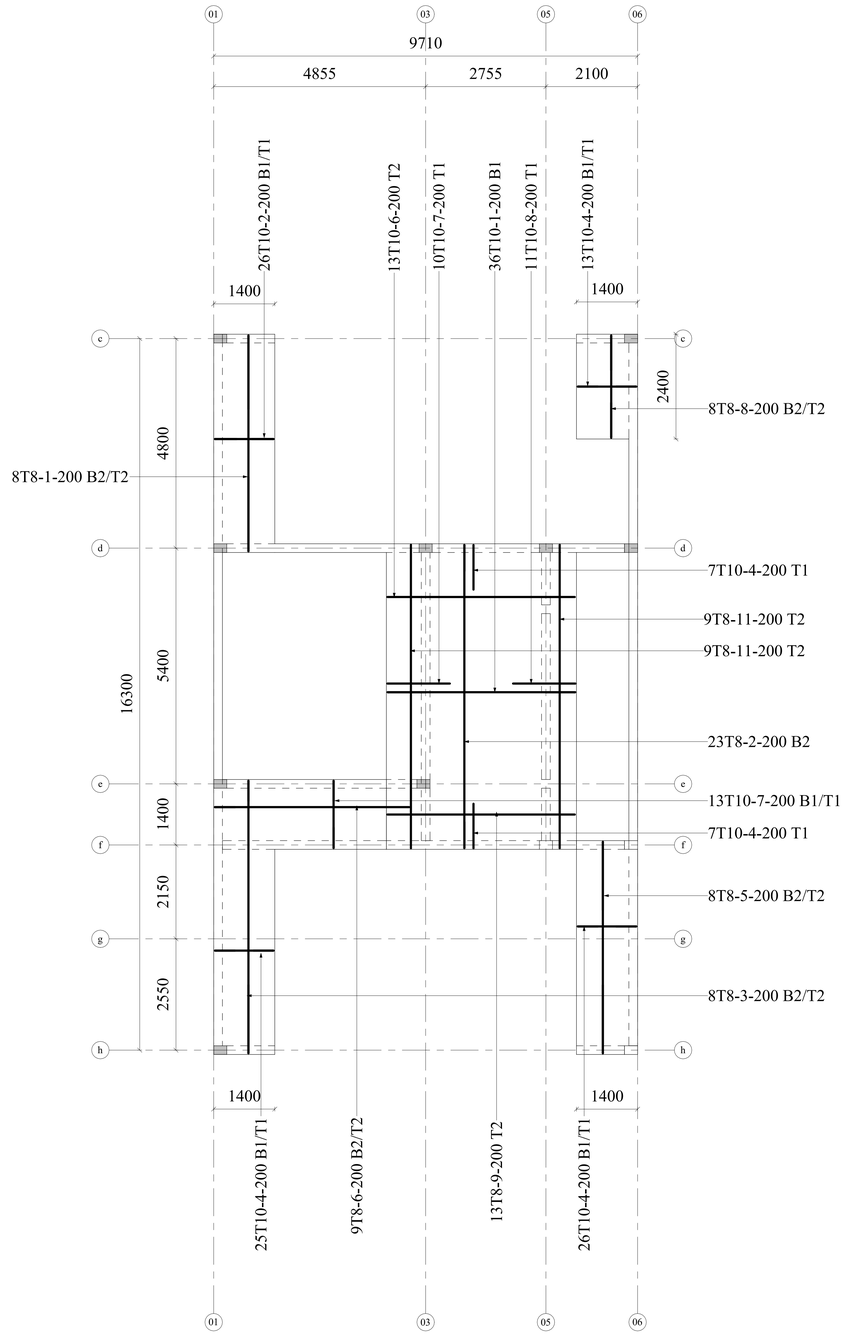

ROOF SLAB REINFORCEMENTS

1 : 50

GENERAL STRUCTURAL NOTES

1. All dimensions in millimeters.
2. Figured dimensions to be taken from the drawing. Do not scale.
3. All structural drawings are to be read in conjunction with their relevant counterparts, including but not limited to architectural, mechanical, electrical and plumbing drawings. Any discrepancy to be reported to the Engineer immediately.
4. All excavations are to be approved by the Civil and Structural Engineer(s).
5. Concrete to be class C20/25 with a minimum cube crushing strength of 18N/mm^2 and 25N/mm^2 at 7 days and 28 days respectively.
6. Blinding concrete to be class C15 with a minimum crushing strength of 15N/mm^2 at 28 days.
7. The minimum cover to reinforcement:
   - Foundations : 50mm
   - Columns : 40mm
   - Beams : 25mm
   - Slabs : 25mm
8. Hoop Iron to be placed on every other course of masonry walls and bonded to the reinforced concrete columns.
9. All reinforcement works to be inspected and approved by the Engineer before concreting.
10. Minimum spacing between longitudinal bars not less than 25mm.
11. Minimum spacing between transverse bars not less than 150mm c/c.
12. All segment lengths to be rounded up by 5mm and all cutting lengths to be rounded up by 50mm.
13. Reinforcement lap lengths to be 50 x Diameter of the smaller lapped bar.
    - T8 - 400mm
    - T10 - 500mm
    - T12 - 600mm
    - T16 - 800mm
    - T20 - 1000mm
    - T25 - 1200mm
    - T32 - 1600mm
14. Masonry crushing strength to be 7 N/mm^2.
15. Compaction is to be done in layers not exceeding 150mm in thickness.
16. Waterproofing of Structures

- Approved and guaranteed waterproofing systems all as detailed shall be provided to the following structures:
  - Water tank slab

General Abbreviations as follows:

T - Top Bar	B - Bottom Bar
T1 - Main Top Bar	T2 - Distribution Top Bar
B1 - Main Bottom Bar	B2 - Distribution Bottom Bar
N.F - Near Face	F.F - Far Face
A/W - Alternating With	E.W. - Each Way

Revision	Description	Date

CLIENT: EVANS KAVISI & LATOYA OUNA


PROJECT: PROPOSED RESIDENTIAL DEVELOPMENT

ARCHITECT: DMS ARCHITECTURE


TITLE: ATTIC FLOOR REINFORCEMENT DETAILS LAYOUTS

ENG. LATOYA OUNA
E694

JOB No. 06	
DRG No. DMS-026-003/STR/02	
Project Date: JUNE 2026	
Sheet Issue Date: 15/06/2026	
DESIGNED: V.N.M	CHECKED BY: ENG. L.O
DRAWN BY: V.N.M	SCALE: As indicated

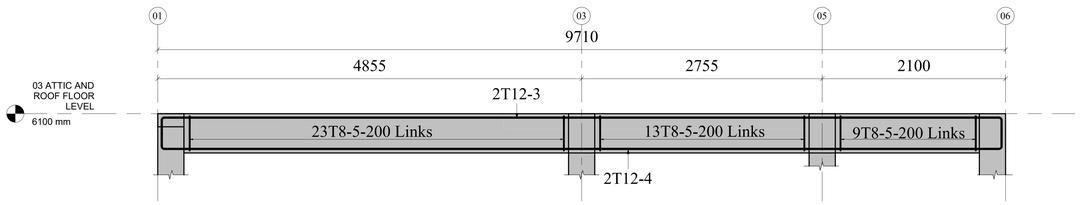

BEAM 10 450 X 200MM
1 : 25

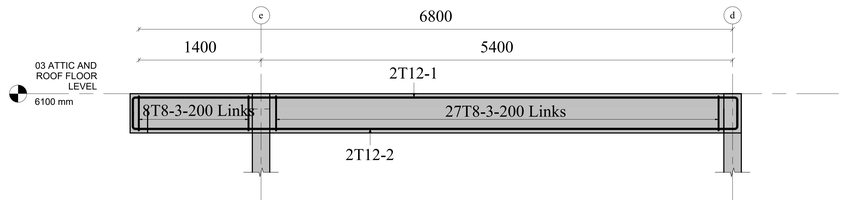

BEAM 11 450 X 200MM
1 : 25

GENERAL STRUCTURAL NOTES

1. All dimensions in millimeters.
2. Figured dimensions to be taken from the drawing. Do not scale.
3. All structural drawings are to be read in conjunction with their relevant counterparts, including but not limited to architectural, mechanical, electrical and plumbing drawings. Any discrepancy to be reported to the Engineer immediately.
4. All excavations are to be approved by the Civil and Structural Engineer(s).
5. Concrete to be class C20/25 with a minimum cube crushing strength of 18N/mm^2 and 25N/mm^2 at 7 days and 28 days respectively.
6. Blinding concrete to be class C15 with a minimum crushing strength of 15N/mm^2 at 28 days.
7. The minimum cover to reinforcement:
   - Foundations : 50mm
   - Columns : 40mm
   - Beams : 25mm
   - Slabs : 25mm
8. Hoop Iron to be placed on every other course of masonry walls and bonded to the reinforced concrete columns.
9. All reinforcement works to be inspected and approved by the Engineer before concreting.
10. Minimum spacing between longitudinal bars not less than 25mm.
11. Minimum spacing between transverse bars not less than 150mm c/c.
12. All segment lengths to be rounded up by 5mm and all cutting lengths to be rounded up by 50mm.
13. Reinforcement lap lengths to be 50 x Diameter of the smaller lapped bar.


T8 - 400mm	T20 - 1000mm
T10 - 500mm	T25 - 1200mm
T12 - 600mm	T32 - 1600mm
T16 - 800mm	

14. Masonry crushing strength to be 7 N/mm^2.
15. Compaction is to be done in layers not exceeding 150mm in thickness.
16. Waterproofing of Structures


- Approved and guaranteed waterproofing systems all as detailed shall be provided to the following structures:
  - Water tank slab

General Abbreviations as follows:


T - Top Bar	B - Bottom Bar
T1 - Main Top Bar	T2 - Distribution Top Bar
B1 - Main Bottom Bar	B2 - Distribution Bottom Bar
N.F - Near Face	F.F - Far Face
A/W - Alternating With	E.W. - Each Way

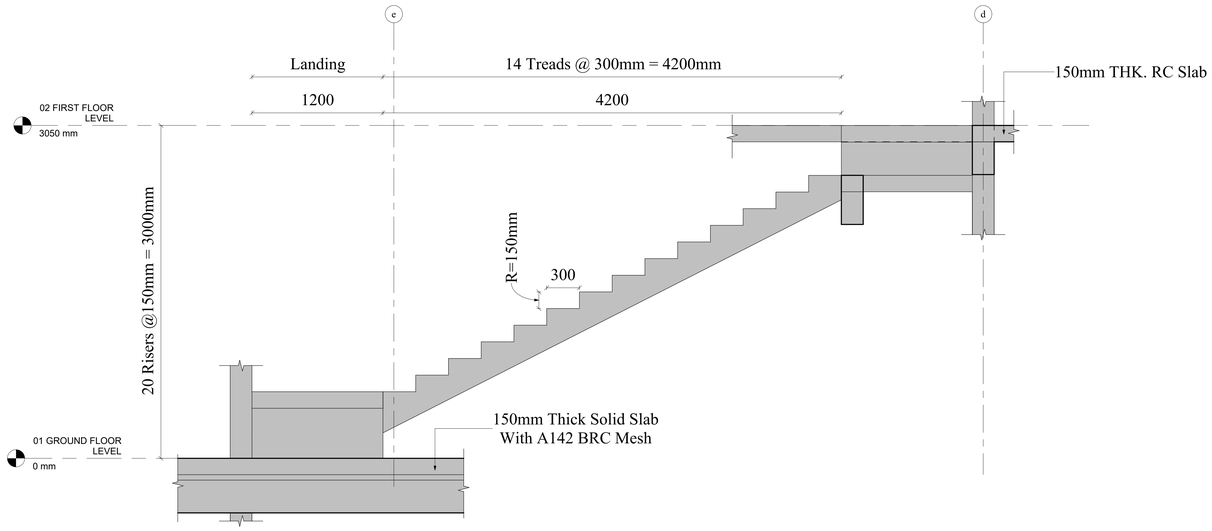


STAIRCASE DETAILS
1 : 20

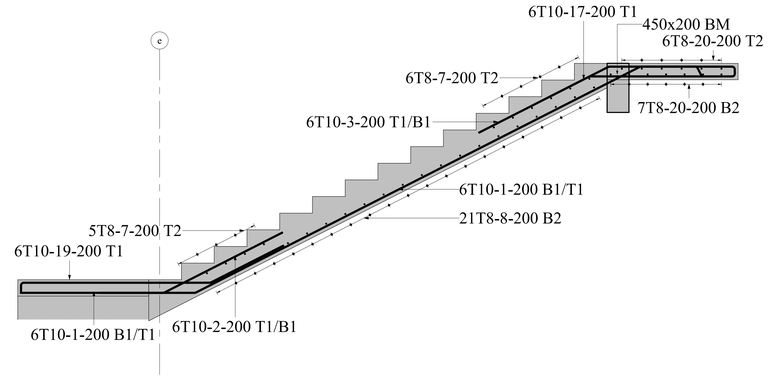

FLIGHT 2 REINFORCEMENT DETAILS
1 : 20

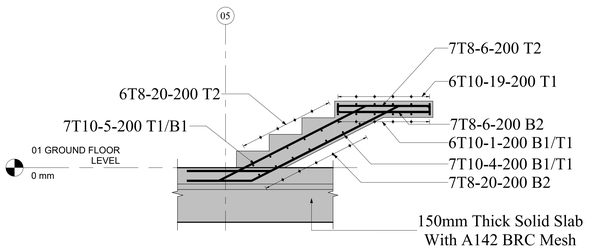

FLIGHT 1 REINFORCEMENT DETAILS
1 : 20

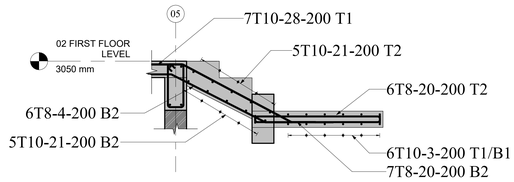

FLIGHT 3 REINFORCEMENT DETAILS
1 : 20

Revision	Description	Date

CLIENT
EVANS KAVISI & LATOYA OUNA


PROJECT
PROPOSED RESIDENTIAL DEVELOPMENT

ARCHITECT
DMS ARCHITECTURE


TITLE
BEAM AND STAIRCASE REINFORCEMENT DETAILS LAYOUTS

ENG. LATOYA OUNA
E694


JOB No. 06
DRG No.DMS-026-003/STR/03
Project Date: JUNE 2026
Sheet Issue Date: 15/06/2026
DESIGNED: V.N.M
CHECKED BY: ENG. L.O
DRAWN BY: V.N.M
SCALE: As indicated

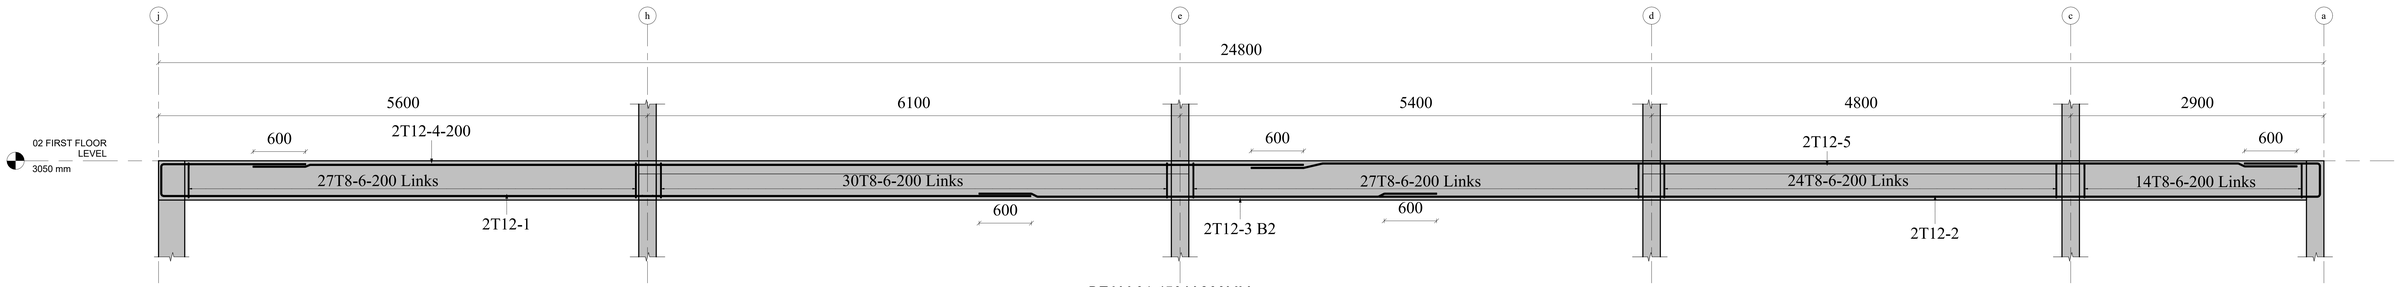


BEAM 01 450 X 200MM
1 : 25

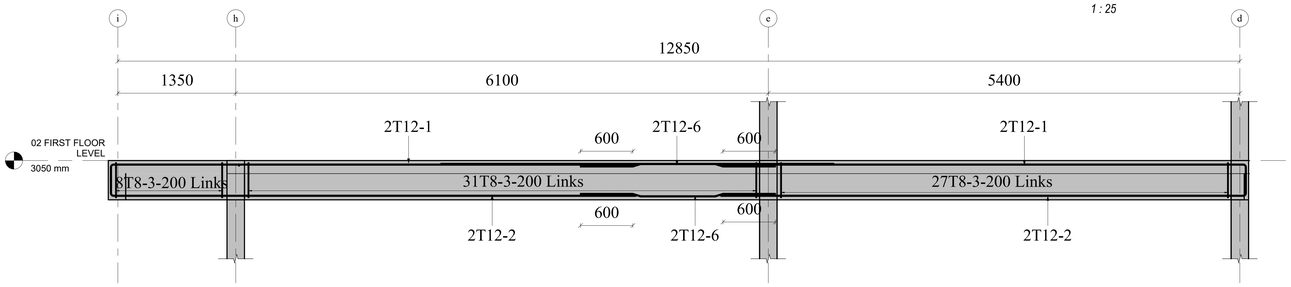


BEAM 02 450 X 200MM
1 : 25

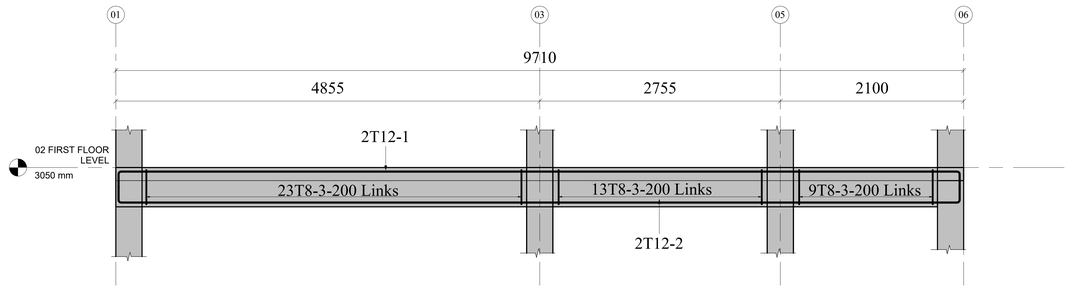


BEAM 03 450 X 200MM
1 : 25

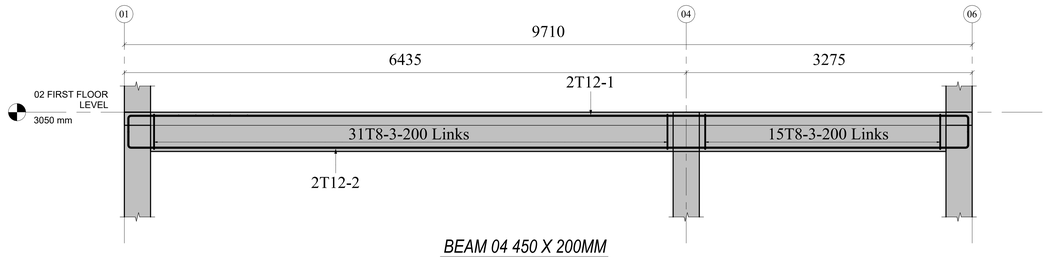


BEAM 04 450 X 200MM
1 : 25

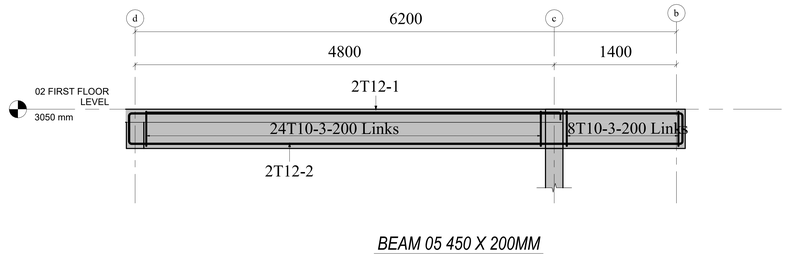


BEAM 05 450 X 200MM
1 : 25

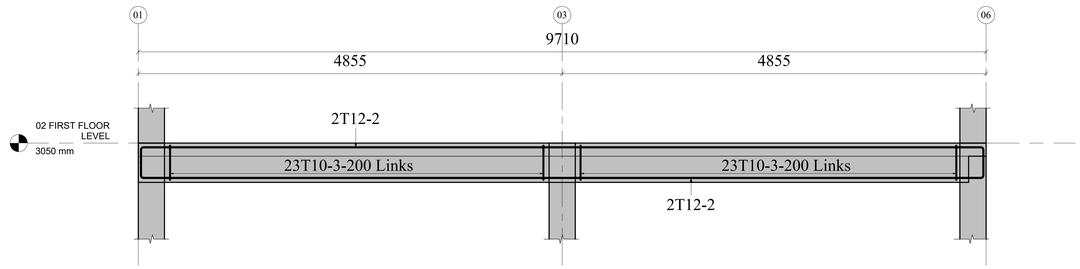


BEAM 06 450 X 200MM
1 : 25

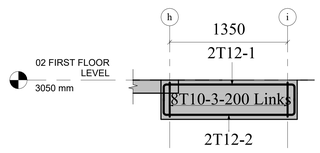


BEAM 07 450 X 200MM
1 : 25

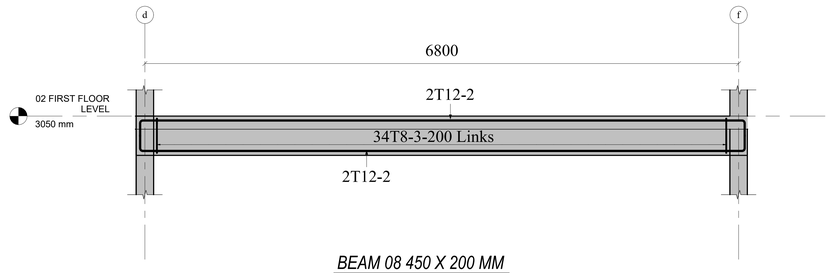

BEAM 08 450 X 200 MM
1 : 25

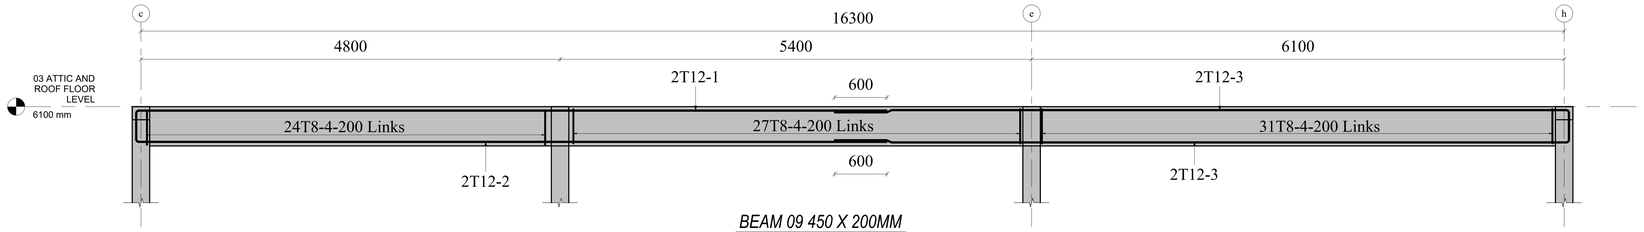

BEAM 09 450 X 200MM
1 : 25

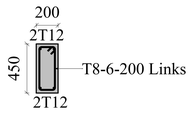

TYPICAL BEAM SECTION
1 : 20

Revision	Description	Date

CLIENT
EVANS KAVISI & LATOYA OUNA

PROJECT
PROPOSED RESIDENTIAL DEVELOPMENT

ARCHITECT
DMS ARCHITECTURE

TITLE
BEAM REINFORCEMENT DETAILS LAYOUTS

ENG. LATOYA OUNA
E694

JOB No. 06	
DRG No. DMS-026-003/STR/04	
Project Date: JUNE 2026	
Sheet Issue Date: 15/06/2026	
DESIGNED: V.N.M	CHECKED BY: ENG. L.O
DRAWN BY: V.N.M	SCALE: As indicated