
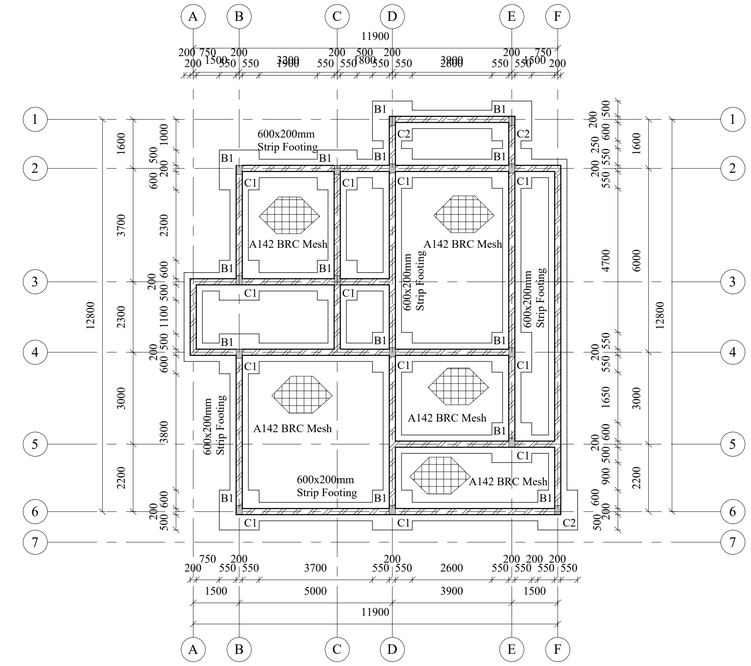



FOUNDATION LAYOUT- STRIP FOOTING AND COLUMN BASES

1 : 100

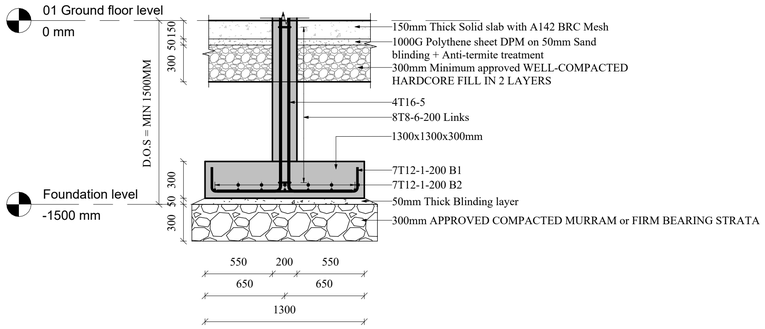


TYPICAL COLUMN BASE 1500 X1500 MM (15NO.)

1 : 25

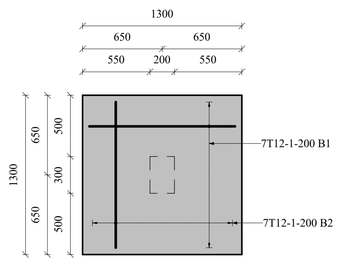


TYPICAL 1500 X1500 MM COLUMN BASE PLAN

1 : 25

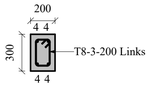


TYPICAL COLUMN SECTION 02-02

1 : 25

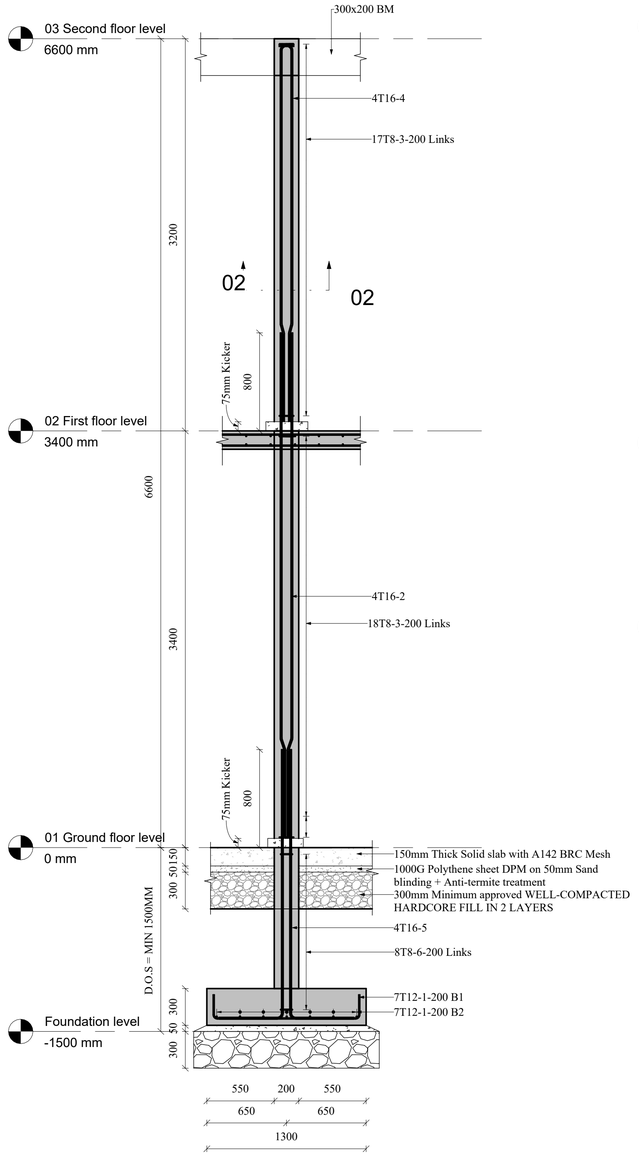


TYPICAL COLUMN C1 300 X 200 MM (12NO.)

1 : 25

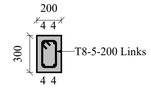


TYPICAL COLUMN SECTION 01-01

1 : 25

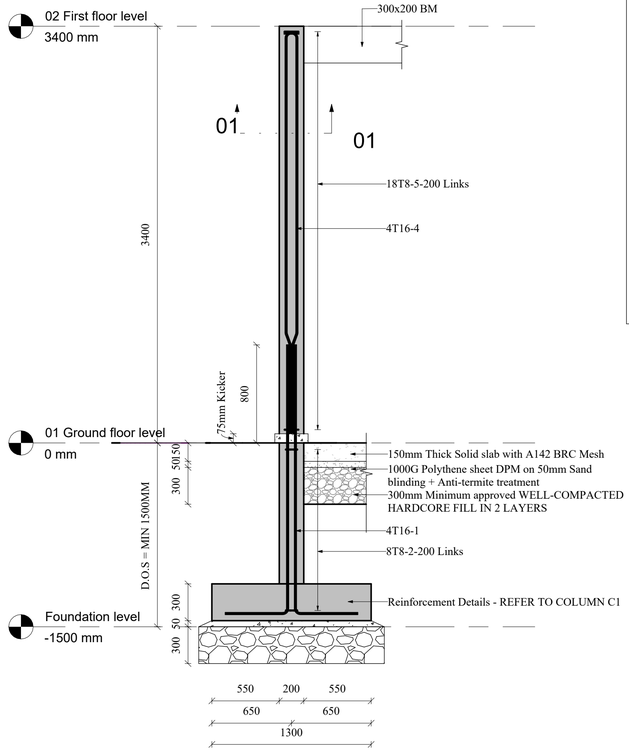

TYPICAL COLUMN C2 300 X 200 MM (3 NO.)

1 : 25

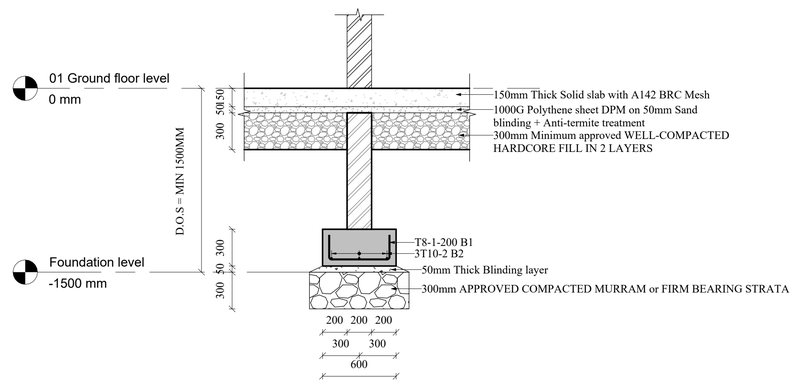

STRIP FOOTING SECTION

1 : 25

GENERAL STRUCTURAL NOTES

1. All dimensions in millimeters and levels in meters unless otherwise stated
2. Figured dimensions to be taken from the drawing
3. All Structural drawings to be read in conjunction with Architectural drawings and all dimensions to be verified. Any discrepancy to be reported to the Engineer immediately
4. Concrete to be class C20/25 with a minimum cube crushing strength of 18N/mm^2 and 25N/mm^ at 7 days and 28 days respectively.
5. Hoop Iron to be placed on every other course of masonry walls and bonded to the reinforced concrete columns
6. All reinforcement works to be inspected and approved by the Engineer before concreting
7. Minimum spacing between longitudinal bars not less than 25mm
8. Minimum spacing between transverse bars not less than 150mm c/c
9. All segment lengths to be rounded up by 5mm and all cutting lengths to be rounded up by 25mm
10. Reinforcement lap lengths to be 50 x Diameter of the smaller lapped bar

General Abbreviations as follows:

1. T - Top Bar
2. B - Bottom Bar
3. T1 - Main Top Bar
4. T2 - Distribution Top Bar
5. B1 - Main Bottom Bar
6. B2 - Distribution Bottom Bar
7. N.F - Near Face
8. F.F - Far Face
9. A/W - Alternating With
10. E.W. - Each Way

CONCRETE STRENGTH

1. Foundation Bases - Class 30
2. Columns (Basement 02 - First Floor) - Class 30
3. All Floor Slabs and Beams - Class 30

Consultants	+211 919 962243 +254 720 962243 +254 703 628720 telepathystudios@gmail.com	Project title: Townhouse in Hai Kasire_Juba, SSD	CLIENT:

Drawing title: FOUNDATION LAYOUT-STRIP FOOTING &COLUMN BASES

JOB No. SSD PR_4

Sheet Issue Date: 08/08/26


Drawn: V.N.M

SCALE: As indicated

Date: AUGUST 2026


Project Architects: K. Roman & S. Saruni

This drawing is the copyright of the be reproduced without license. DO NOT scale from this Drawing

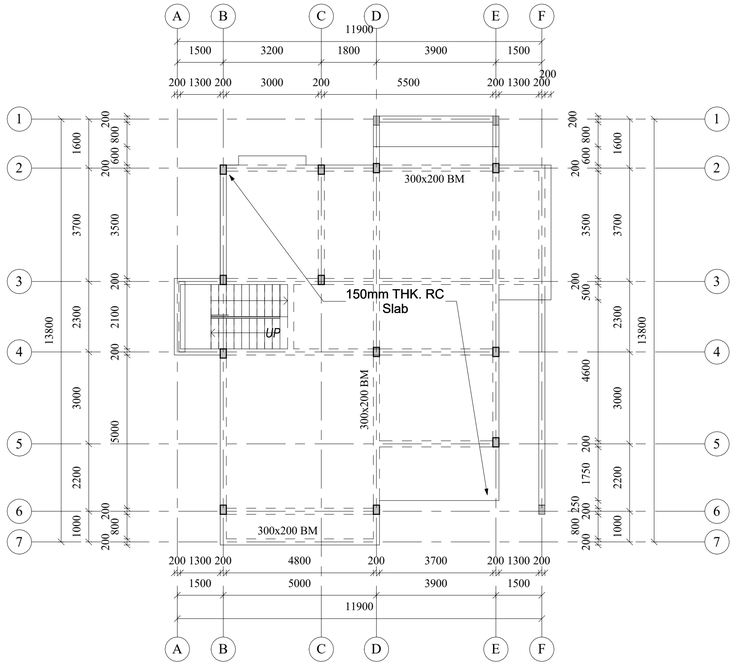


GROUND FLOOR BEAM LAYOUT

1 : 100

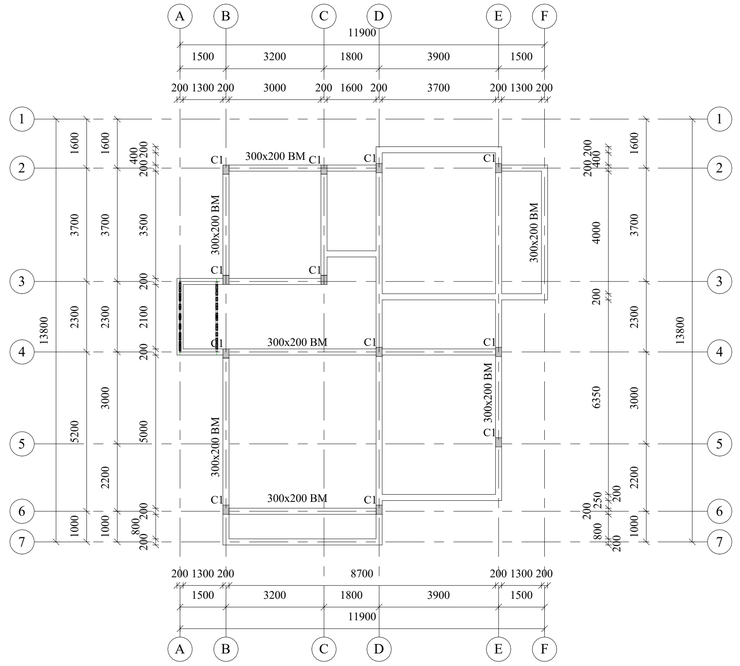


FIRST FLOOR BEAM LAYOUT

1 : 100

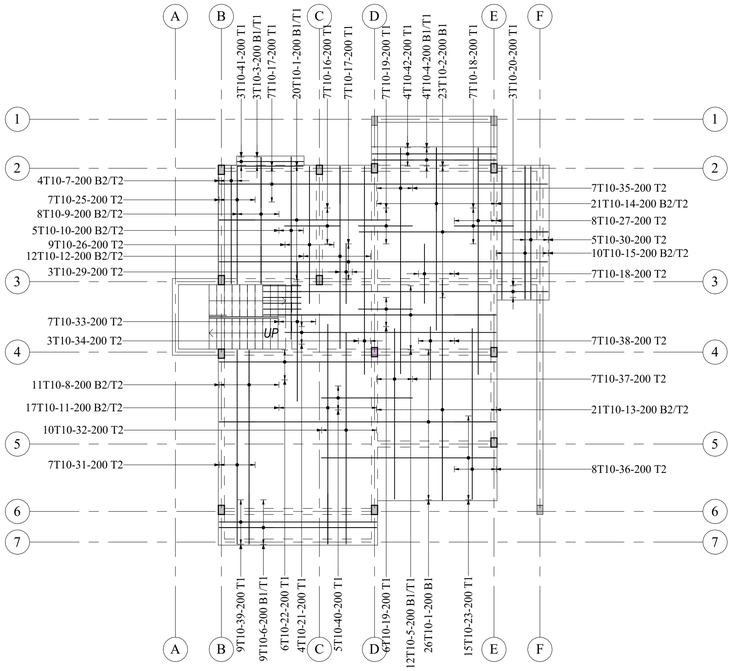

FIRST FLOOR SLAB REINFORCEMENTS

1 : 100

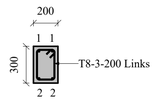

TYPICAL BEAM SECTION

1 : 25

GENERAL STRUCTURAL NOTES

1. All dimensions in millimeters and levels in meters unless otherwise stated
2. Figured dimensions to be taken from the drawing
3. All Structural drawings to be read in conjunction with Architectural drawings and all dimensions to be verified. Any discrepancy to be reported to the Engineer immediately
4. Concrete to be class C20/25 with a minimum cube crushing strength of 18N/mm^2 and 25N/mm^ at 7 days and 28 days respectively.
5. Hoop Iron to be placed on every other course of masonry walls and bonded to the reinforced concrete columns
6. All reinforcement works to be inspected and approved by the Engineer before concreting
7. Minimum spacing between longitudinal bars not less than 25mm
8. Minimum spacing between transverse bars not less than 150mm c/c
9. All segment lengths to be rounded up by 5mm and all cutting lengths to be rounded up by 25mm
10. Reinforcement lap lengths to be 50 x Diameter of the smaller lapped bar

General Abbreviations as follows:
1. T - Top Bar
2. B - Bottom Bar
3. T1 - Main Top Bar
4. T2 - Distribution Top Bar
5. B1 - Main Bottom Bar
6. B2 - Distribution Bottom Bar
7. N.F - Near Face
8. F.F - Far Face
9. A/W - Alternating With
10. E.W. - Each Way

CONCRETE STRENGTH
1. Foundation Bases - Class 30
2. Columns (Basement 02 - First Floor) - Class 30
3. All Floor Slabs and Beams - Class 30

Consultants

telepat
Telepathy Studios Ltd
Teleporting your dreams into reality

+211 919 962243
+254 720 962243
+254 703 628720
telepathystudios@gmail.com

Project title:

Townhouse in Hai Kasire_Juba, SSD

CLIENT:

Drawing title:

GROUND FLOOR AND FIRST FLOOR BEAM LAYOUT & FIRST FLOOR SLAB REINFORCEMENTS

JOB No. SSD PR_4

Sheet Issue Date: 08/08/26


Drawn: V.N.M

SCALE: As indicated

Date: AUGUST 2026


Project Architects: K. Roman & S. Saruni

This drawing is the copyright of the be reproduced without license. DO NOT scale from this Drawing

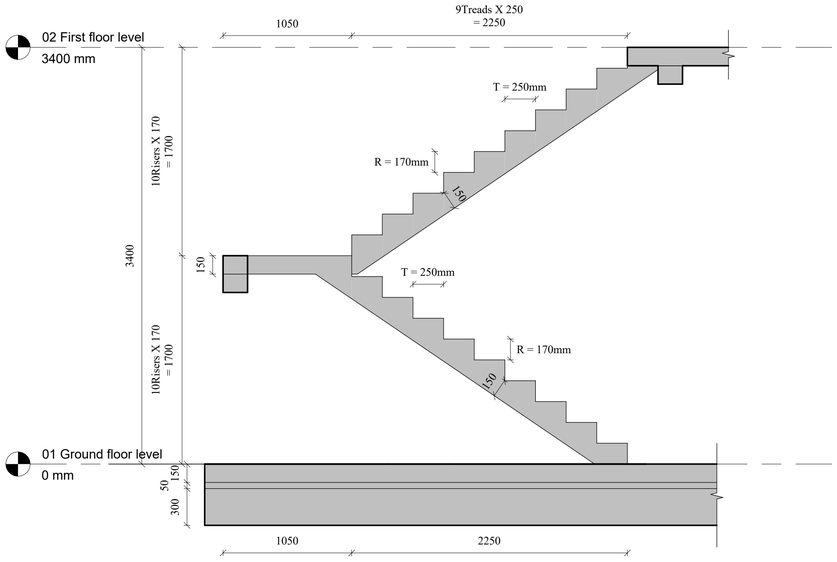

STAIRCASE FLIGHT

1 : 25

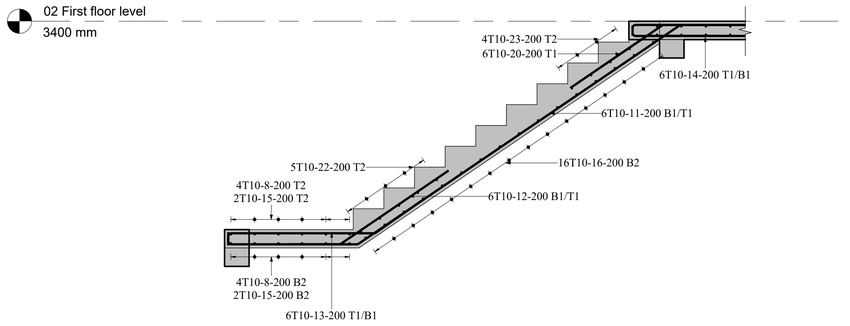

STAIRCASE FLIGHT 2- REINFORCEMENTS


1 : 25

GENERAL STRUCTURAL NOTES

1. All dimensions in millimeters and levels in meters unless otherwise stated
2. Figured dimensions to be taken from the drawing
3. All Structural drawings to be read in conjunction with Architectural drawings and all dimensions to be verified. Any discrepancy to be reported to the Engineer immediately
4. Concrete to be class C20/25 with a minimum cube crushing strength of 18N/mm^2 and 25N/mm^ at 7 days and 28 days respectively.
5. Hoop Iron to be placed on every other course of masonry walls and bonded to the reinforced concrete columns
6. All reinforcement works to be inspected and approved by the Engineer before concreting
7. Minimum spacing between longitudinal bars not less than 25mm
8. Minimum spacing between transverse bars not less than 150mm c/c
9. All segment lengths to be rounded up by 5mm and all cutting lengths to be rounded up by 25mm
10. Reinforcement lap lengths to be 50 x Diameter of the smaller lapped bar

General Abbreviations as follows:
1. T - Top Bar
2. B - Bottom Bar
3. T1 - Main Top Bar
4. T2 - Distribution Top Bar
5. B1 - Main Bottom Bar
6. B2 - Distribution Bottom Bar
7. N.F - Near Face
8. F.F - Far Face
9. A/W - Alternating With
10. E.W. - Each Way

CONCRETE STRENGTH
1. Foundation Bases - Class 30
2. Columns (Basement 02 - First Floor) - Class 30
3. All Floor Slabs and Beams - Class 30

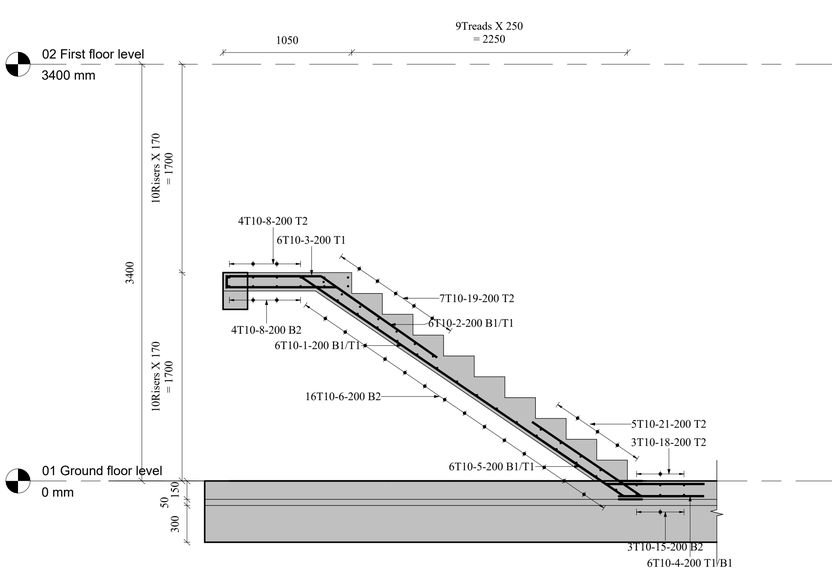

STAIRCASE FLIGHT 1- REINFORCEMENTS

1 : 25

Consultants

telepat
Telepathy Studios Ltd
Teleporting your dreams into reality

+211 919 962243
+254 720 962243
+254 703 628720
telepathystudios@gmail.com

Project title:

Townhouse in Hai Kasire_Juba, SSD

CLIENT:

Drawing title:

STAIRCASE DETAILS

JOB No.
SSD PR_4

Sheet Issue Date: 08/08/26

Drawn: V.N.M

SCALE: As indicated

Date: AUGUST 2026

Project Architects:
K. Roman & S. Saruni

This drawing is the copyright of the
be reproduced without license. DO NOT scale from this Drawing